Foyer VK-1 — wall drilling template (print at 100 %)

Check: the 100 mm scale bar below must measure exactly 100 mm.

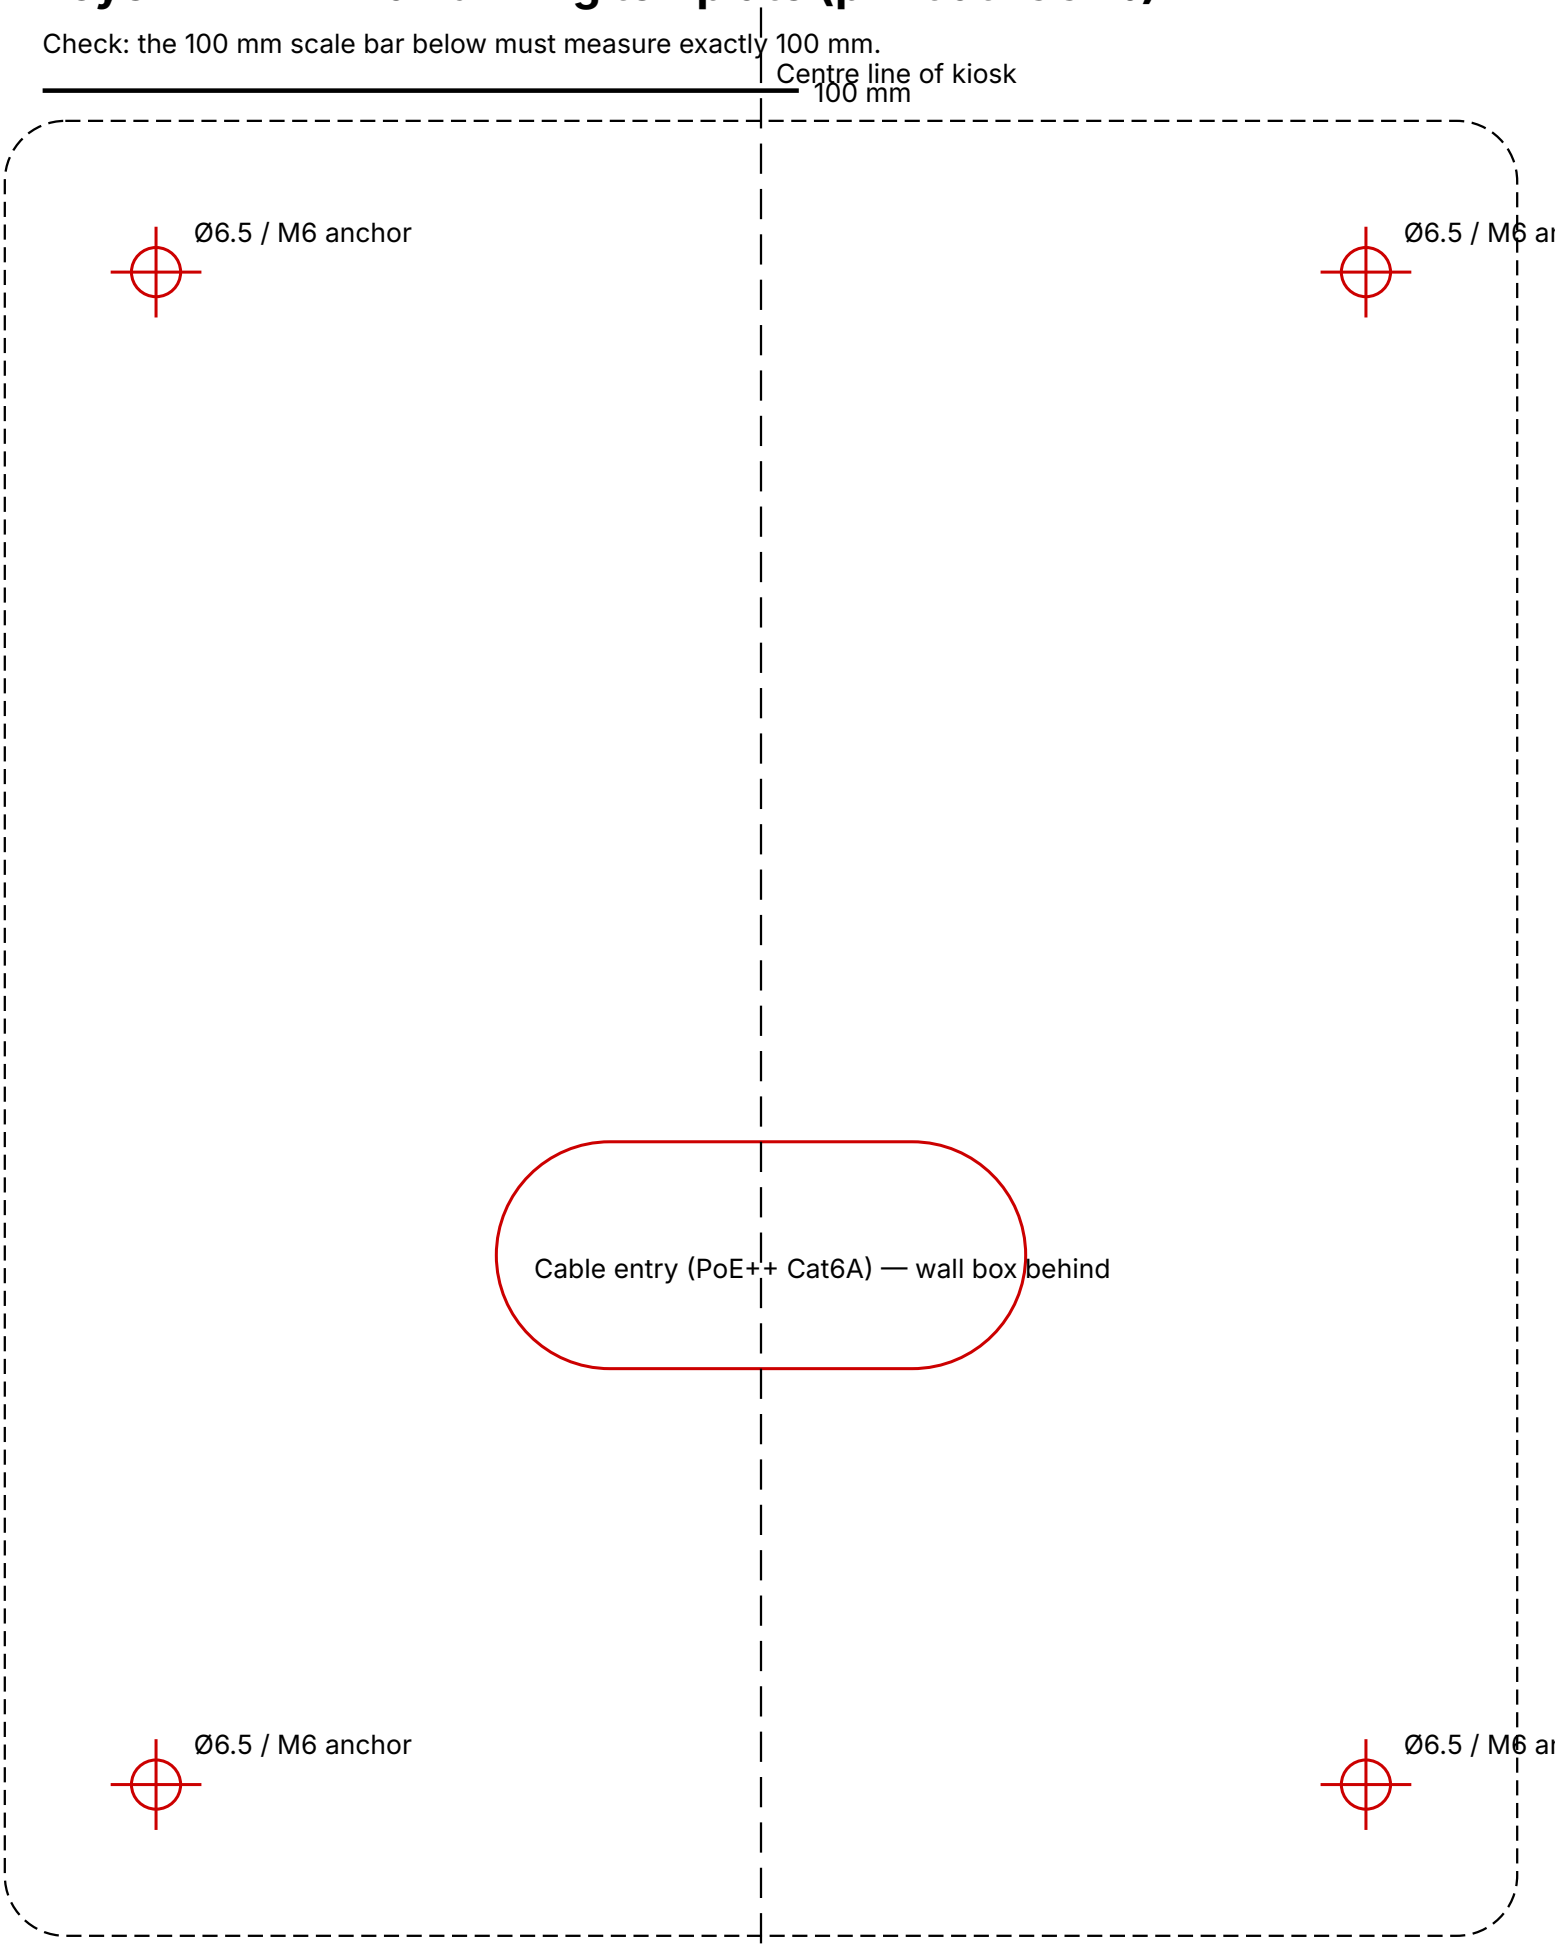

Mount-plate centre is 1096 mm above finished floor (unit base 671 mm; deck front 861 mm, ADA counter height).

Use 4x M6 screws into studs, or M6 metal cavity anchors (min. 4 × 500 N). Level before tightening.